הנגשת מקומות להתקהלות

דרישת חוק	יישום
נדרש להציב מערכת שמע על כל סוג דלפק: קבלה / מכירות /פוד טראק / בר	
יש להתקין שילוט הכוונה לכל הפונקציות במקום לרבות: חניות נגישות, כניסה נגישה, תאים נגישים, דרך נגישה, מקומות צפיה וכו'	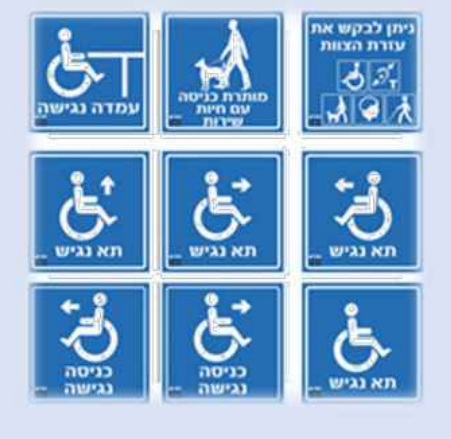
תוספ מערכת עזר לשמיעה הכוללת 2 שליש אוזניות והייתר לולאות השראה (מכמות המוזמנים). עד 1000 איש- 5% מ 1001-10.000- 3%+50 יח' מעל 10,000- 1%+320 יח' במידה והמערכת היא מסוג לולאת השראה, יסופקו מקלטים בשיעור של 1% מתפוסת המקום או המושבים ולפחות שניים.	
עמדות צפייה 0.80 1.20 אמ'	

עד600	1 ל150 מ'ומות ישיבה ולא פחות מ4
600-1000	6 ועוד 1% מסך כל מקומות הישיבה
1000-3000	4 ועוד 1% מסך כל מקומות הישיבה
3000-10,000	28 ועוד 0.5% מסך כל מקומות הישיבה
מעל 10,000	63 ועוד 0.25% מסך כל מקומות הישיבה

דרישת חוק	יישום
תאים נגישים 	בתי שימוש נגישים במקומות להתקהלות 8.147 (א) במקומות להתקהלות יהיה מספר בתי השימוש הנגישים על פי מספר מקומות הישיבה המיוחדים וכמפורט בטבלה להלן

מספר מקומות ישיבה מיוחדים	מספר בתי שימוש נגישים נדרשים
12-0	לפי האמור בפרט 8.146
13-24	3 שמתוכם 1 משותף לשני המינים
25-40	4 שמתוכם 1 משותף לשני המינים
41-60	5 שמתוכם 2 משותפים לשני המינים
61 ומעלה	5 ועוד 1 לכל 20 מקומות מיוחדים נוספים מעל 61

דרישת חוק	יישום
אספקת כרטיסים	יש לשריין מקומות מיוחדים עד שבוע לפני האירוע, עד 20 דק' לפני הקרנת סרט, ועד זמן סביר לפני כל אירוע אחר.
כתוביות בסרטים בשפת הסרט	בהצפה של הקרנה מסחרית של סרט בעברית או אנגלית (ב70% לפחות מעותקי הסרט)
תרגום לשפת הסימנים	במידה והאירוע מילולי בעיקרו, יש לספק לבקשת אדם עם מוגבלות תרגום לשפת סימנים. ניתן לפטור במידה ולא הוגשו בקשות, או נעשה מאמץ סביר למצוא מתרגם. החייב פטור אם מוקרן סרט. אירוע סגור עם תפוסה של עד 150 איש. אם האירוע אינו מילולי בעיקרו. קהל מזדמן ללא מושבים.

דרישת חוק	יישום
כסאות נגישים-10% מסך המושבים במקום	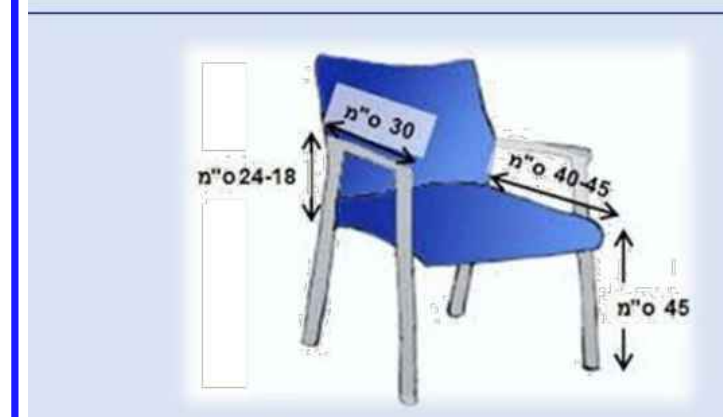 30 ס"מ 40-45 ס"מ 18-24 ס"מ 45 ס"מ
פרסום האירוע	יש לפרסם במדיה את היות האירוע מונגש טרם קיומו עד שבוע לפני קיומו לרבות: דרכי הגעה, חניות, כניסות לאירוע, מקומות צפייה מיוחדים קיום מערכות שמע ו/או תרגום לשפת הסימנים, תאי שירותים נגישים, דוכנים, קופות נגישות וכו'
תמלול	ניתן באמצעות שלט אלקטרוני או על גבי מסך הקרנה ככל שאופי האירוע ונסיבות העניין מאפשרות זאת. החייב פטור במידה ו: מוקרן סרט. אירוע סגור עם תפוסה של עד 150 איש. אירוע מילולי בעיקרו. רק אם הנסיבות מאפשרות קריאת טקסט. מופע רחוב לקהל מזדמן ללא מושבים.
חניה נגישה	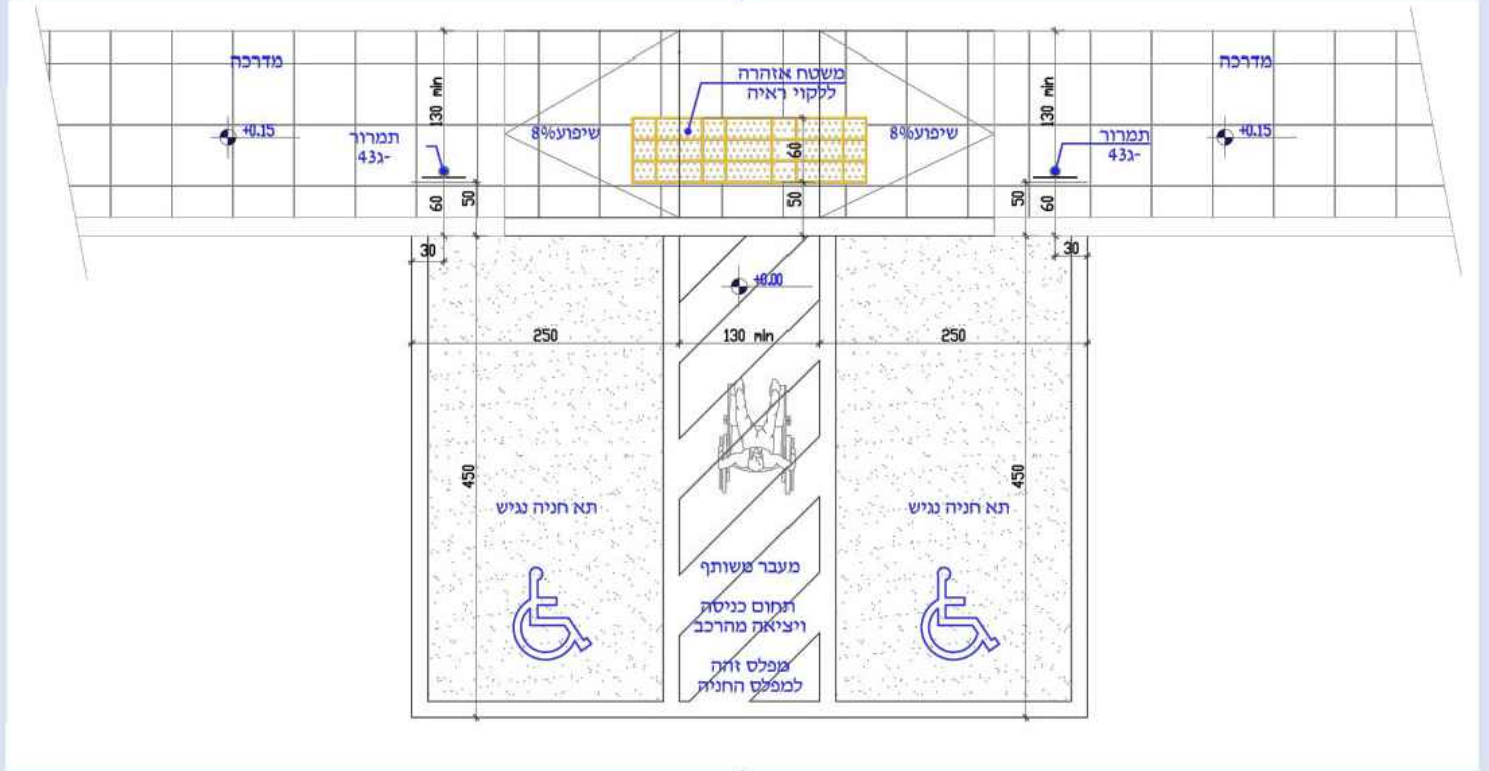 מדרכה משטח אזהרה לקלוי ראייה שיפוע 8% תמרור 433- תא חניה נגיש מעבר משותף תחום כניסה ויציאה מהרכב מפלס זהה למפלס החניה
מדרגות וכבשים	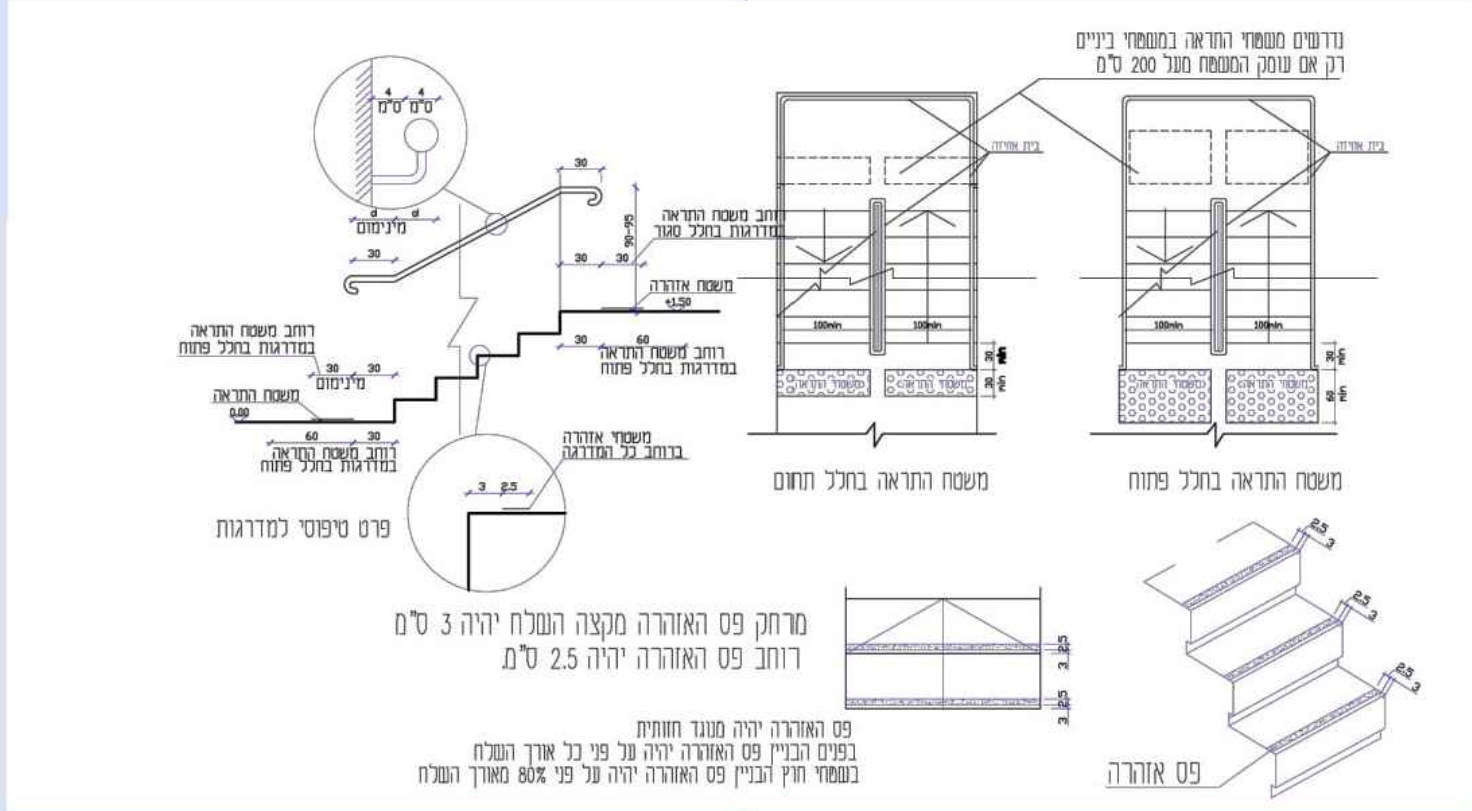 משטח התראה בחלל פתוח משטח התראה בחלל תחום פרט טיפוסי למדרגות פס אזהרה מרחק פס האזהרה מקצה השלח יהיה 3 ס"מ רוחב פס האזהרה יהיה 2.5 ס"מ
דלפק נגיש	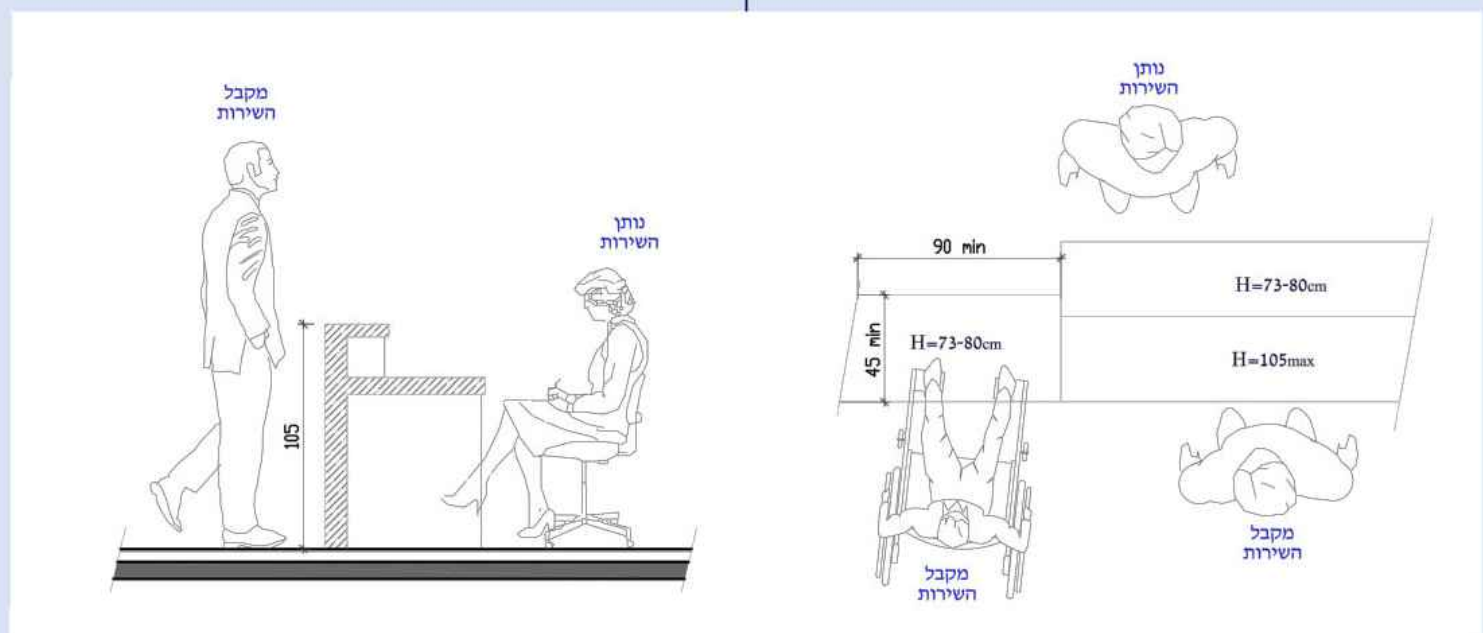 מקבל השירות נותן השירות 90 min H=73-80cm H=105max 105

חישוב מרחק בין יציאות	
אלכסון שטח האירוע	125
שליש האלכסון	41.6
מרחק קיים בין יציאות	118 תקין

ריכוז חישובי תפוסת קהל ודרכי מוצא

תיאור השימוש בקומה או חלק מהקומה	שטח ברוטו (מ"ר)	שטח נטו (מ"ר)	מקדם תפוסה מ"ר/נפש לפי פרק ב' סימן י"ב טבלה 3.2.12.2	סה"כ תפוסה אפשרית	סה"כ תפוסה רצויה לחישוב פתחים	כמות כניסות יציאות נדרשות: כמות	רוחב	מקדמי תפוסה נדרשים ע"פ רשות הכבאות	יציאות וכניסות מתוכננות: כמות	רוחב	סהכ רוחב פתחים	האם עונה על הדרישה
התקהלות שטח כללי	5200	2900	1	לפי שטח צפייה 1200 איש	1200 איש	3 יציאות	220 סמ כל אחד	סהכ רוחב פתחים נדרש סמ	3 יציאות	220 סמ כל אחד	סמ	כן
						2 כניסות	110 סמ כל אחד		3 כניסות	110 סמ כל אחד		

עד 1000 איש - 1 כניסה 21 יציאות
עד 2000 איש - 2 כניסות 31 יציאות
עד 3000 איש - 3 כניסות 41 יציאות
וכו...

תפוסה	מדרגות	רוחב/כבש
עד 2000 איש	0.8	0.5
2000-5000 איש	0.762	0.508
5000-10000 איש	0.508	0.381
מעל 10000 איש	0.300	0.254

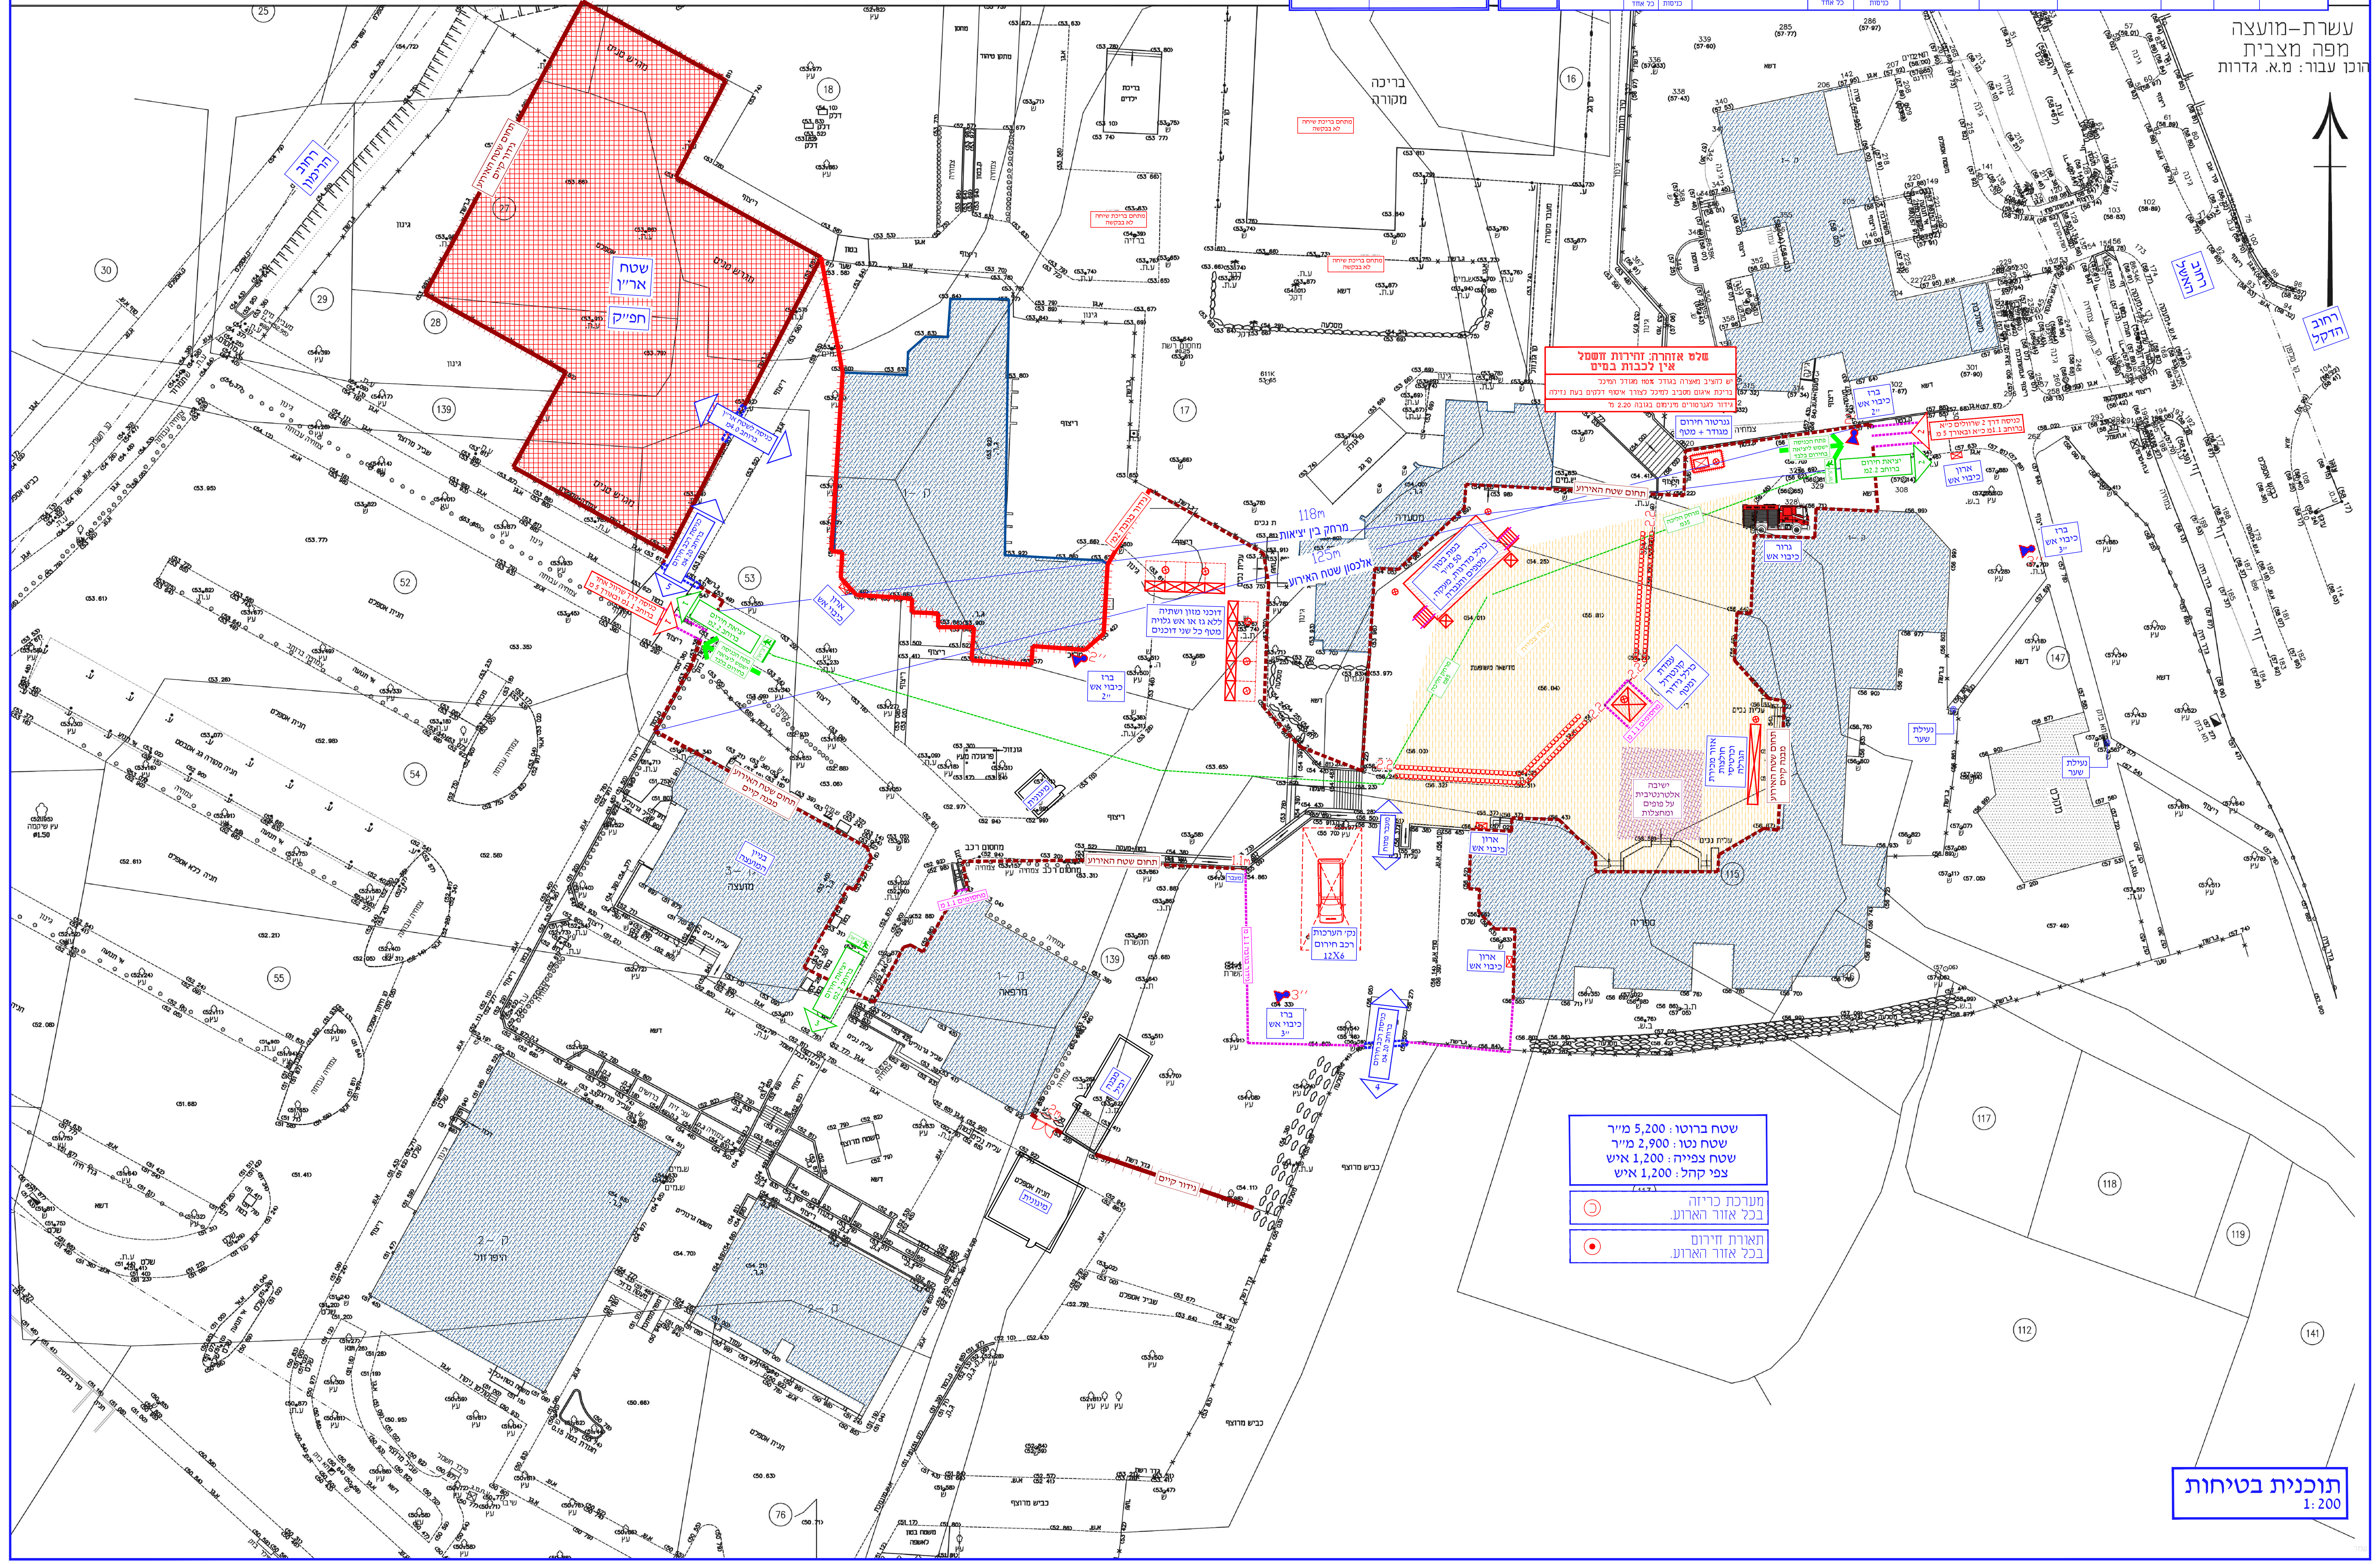
עשרת-מועצה
מפה מצבית
הוכן עבור: מ.א. גדרות
רחוב הרימון
רחוב האשל
רחוב הדקל
שטח אר"ן
חפ"ק
מגרש טניס
כניסה לשטח אר"ן ברוחב 4.0 מ'
תחום שטח האירוע גידור קיים
בריכה מקורה
בריכת ילדים
מתחם בריכת שחיה לא בבקשה
שלט אזהרה: זהירות חשמל אין לכבות במים
יש להציב מאצרה בגודל 110% מגודל המיכל
בריכת איגום מסביב למיכל לצורך איסוף דלקים בעת נזילה
גידור לגנרטורים מינימום בגובה 2.20 מ'
גנרטור חירום מגודר + מטף
118m מרחק בין יציאות
125m אלכסון שטח האירוע
גידור בגובה 2מ'
דוכני מזון ושתיה ללא גז או אש גלויה מטף כל שני דוכנים
במת בטון 50 מ"ר כולל מדרגות מעקה מפתח ומטפים בגבה
עמדת קונטרול כולל גידור ומטף
שטח צפייה
ישיבה אלטרנטיבית על פופים ומחצלות
אזור מכירות חולצות וכרטיסי הגרלה
תחום שטח האירוע מבנה קיים
ברז כיבוי אש 2"
ברז כיבוי אש 3"
ארון כיבוי אש
גרור כיבוי אש
נקי' הערכות רכב חירום 12X6
כניסת רכב חירום ברוחב 4.20 מ'
יציאת חירום ברוחב 2.2 מ'
כניסה דרך שרוול ברוחב 1.1 מ' ובאורך 5 מ'
מחסומים 1.1 מ'
גידור קיים
ספריה
מרפאה
בניין המועצה
מועצה
היפרזול
מתנ"ס
מבנה יבילי
חניית אספלט מיגונית
נעילת שער
תוכנית בטיחות 1:200

שטח ברוטו : 5,200 מ"ר
שטח נטו : 2,900 מ"ר
שטח צפייה : 1,200 איש
צפי קהל : 1,200 איש

מערכת כריזה בכל אזור הארוע.

תאורת חירום בכל אזור הארוע.

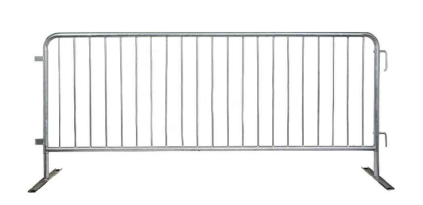
גובה 110 סמ
המרחק המקסימלי בין המוטות הוא 10 סמ
מחסום כניסה – רגלים שטוחות

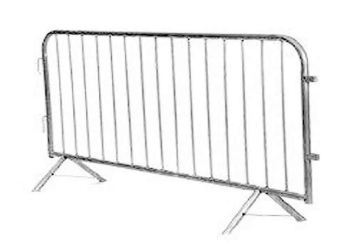
גובה 110 סמ
המרחק המקסימלי בין המוטות הוא 10 סמ
מחסום משטרה

גובה 110 סמ
עם המחסום מחורר, החורים לא יעלו על 8 ממ
מחסום לחץ

תא שירותים כימי נגיש

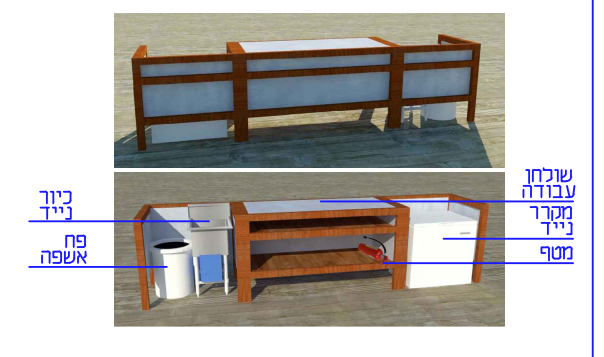
שולחן עבודה
מקרר נייר
מטף
כיור נייך
פח אשפה
דוכן אוכל

גנרטור כולל הארקה
שלט אזהרה
מטפה
גדר בגובה 2מ
כולל שלט אזהרה זהירות חשמל אין לכבות במים
יש להציב מאצרה בגודל 110 אחוז מגודל המיכל
ובריכת איגום מסביב למיכל לצורך איסוף דלקים בעת הניקוז
גנרטור

מקרא

⇔	פתח כניסת ויציאת רכב חירום כולל מידה ומספר הפתח
⇨	פתח כניסה כולל מידה ומספר הפתח
⇦	פתח יציאת חירום כולל מידה ומספר הפתח
יציאה	שלט "יציאה" מואר דו תכליתי בגוון לבן-ירוק (עם חץ או ללא חץ)
▬	גדר קיימת
▬	גדר בגובה 2מ
■■■	גדר מחסומים בגובה 1.1מ
▬	גדר לחץ מול במה במרחק שרשום במידה מהבמה
■■■	מרחק הליכה לפתח יציאת חירום
↔	תוואי נתיב נסיעת רכב חירום
▨	שטח ארן מגודר
▨	איזור חניות נכים
▨	תחום איזור צפייה
▨	מבנה קיים מסביב לשטח האירוע
═	שרוול כניסה ממחסומים בגובה 110 רוחב השרוול לפי המידה שרשומה בפתח הכניסה אורך השרוול 5מ
✳	אזור מואר בתאורה
⊡	מיקום רחבת הערות לרכב חירום בגודל 6מX12מ
☒	פוד טרק כולל מטפה
⊕☒	גנרטור בשיגרה או בחירום כולל מטף וגידור בגובה 2מ כולל שלט אזהרה זהירות חשמל אין לכבות במים יש להציב מאצרה בגודל 110 אחוז מגודל המיכל ובריכת איגום מסביב למיכל לצורך איסוף דלקים בעת הניקוז
☒☒	דוכן לממכר כולל שטח תפעולי אחורי ללא גז או אש גלויה כולל מטפה כל שני דוכנים
▨	במה לפי מידות רשומות כולל הגברה, מדרגות , מאחז יד , מעקות בצידי הבמה גשר תאורה עליון , גב במה אחורי
▭	במה למסך הקרנה לפי מידות רשומות כולל מסך לפי מידות רשומות
▢▢▢	כסאות מול במה במידות 45X50 מעבר ברוחב 45 סמ
☒☒	תאי שירותים כימים לפי כמות רשומה כולל תאים נגישים
☆	זיקוקים המיקום יאושר על ידי משטרת ישראל
אש	עמדת כיבוי אש המכיל: ברז כיבוי אש 2"+ גלגלון 3\4" עם ברז פתיחה מהירה+ 2 זרנוקים 15 מ, כל אחד+ מטף כיבוי אבקה או ש"ע מאושר במשקל 6 ק"ג בתוך ארון תיקני במידות 120*30*80 ס"מ
☰	גלגלון כיבוי אש 3/4" מתאים לת"י 2206 חלק 1.
2"	ברז כיבוי אש בקוטר 2" על זקף 3" עם מחבר שטורץ
3'	ברז כיבוי אש חיצוני בקוטר 3" על זקף 4" עם מחבר שטורץ
▼	ברז כיבוי אש חיצוני כפול בקוטר 3" על זקף 4"/6" עם מחבר שטורץ
⊗	מטפה כיבוי ידני באבקה יבשה במשקל 6 ק"ג או שווה ערך לדליקות מסוג (א,ב,ג) תקני
ג	אזור מוגן ע"י מערכת גלאי אש ועשן מתוכננת עפ"י ת"י 1220, חלק 3.
◯	אזור מכוסה ע"י מערכת כריזה תקנית
⦿	אזור מכוסה ע"י תאורת חירום תקינה

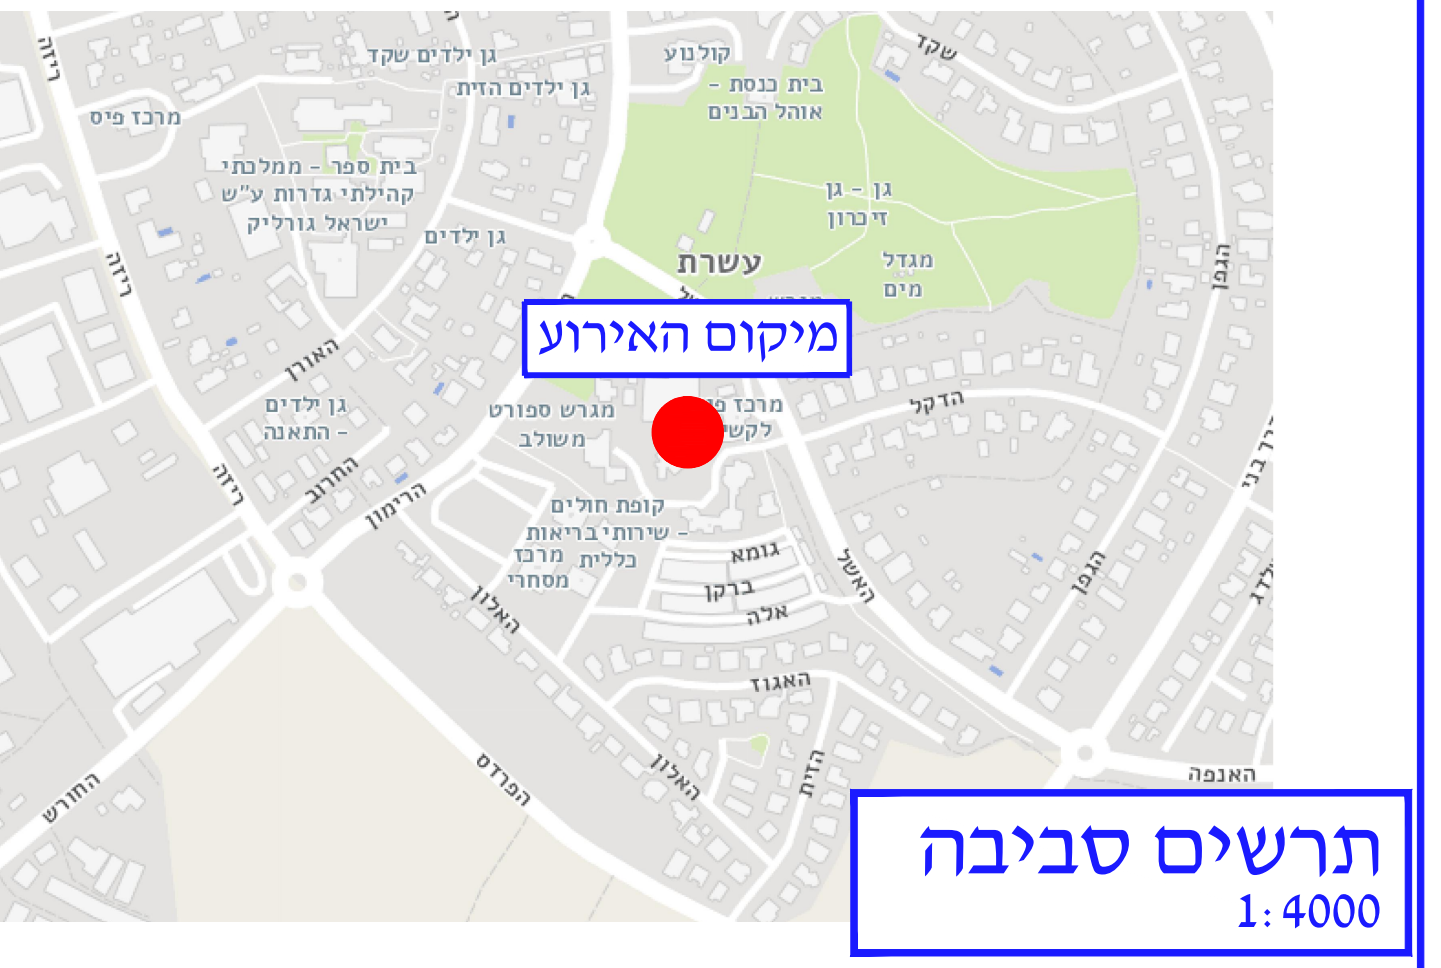
מיקום האירוע
עשרת
גן ילדים שקד
גן ילדים הזית
קולנוע
בית כנסת - אוהל הבנים
מרכז פיס
בית ספר - ממלכתי קהילתי גדרות ע"ש ישראל גוריליק
גן - גן זיכרון
מגדל מים
גן ילדים
מגרש ספורט משולב
קופת חולים - שירותי בריאות כללית מרכז מסחרי
הרימון
הדקל
האשל
הגפן
גומא
ברקן
אלה
האגוז
האנפה
הפרדס
הזית
האורן
החורש
רדידה
התאנה
תרשים סביבה
1: 4000

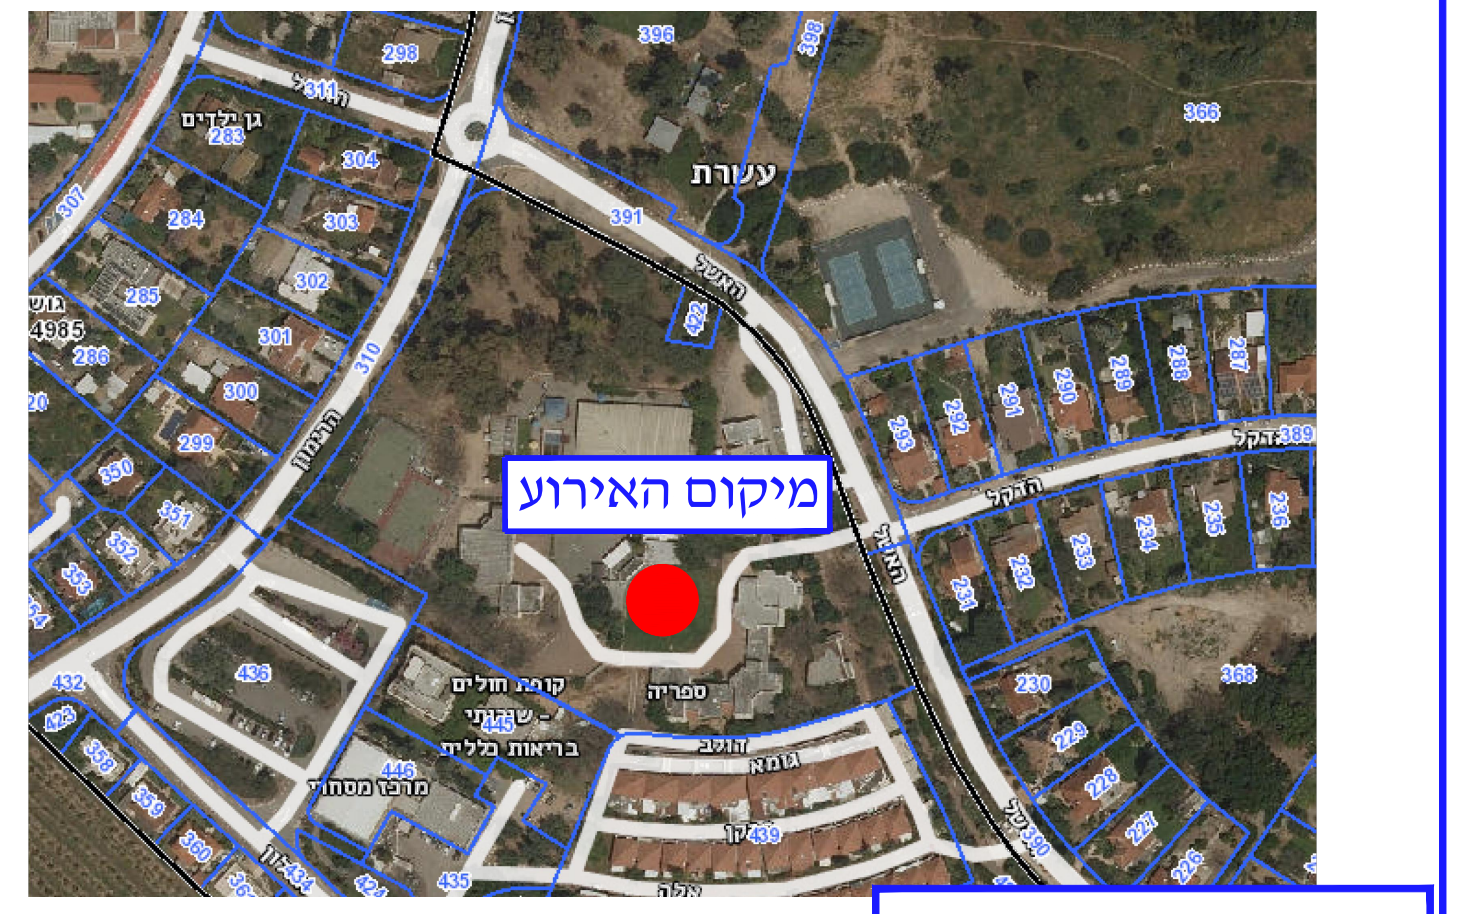
מיקום האירוע
עשרת
גן ילדים
הרימון
האשל
הדקל
ספריה
קופת חולים - שירותי בריאות כללית
מרכז מסחרי
גומא
אלה
תרשים סביבה
1: 2000

תכנית בטיחות

אירוע פסטי-ליונס
יישוב עשרת

דרישות בטיחות באירוע המוני:

- אישור קונסטרוקטור לאלמנטים
- אישור מהנדס מכונות למתקני הרמה
- אישור מתקני משחק ע"פ ת"י 1498
- אישור מתקני ספורט ע"פ ת"י 5515
- אישור מתקני כושר ע"פ ת"י 1497
- אישור למתנפחים ע"פ ת"י 5378
- אישור למתקני יריד ת"י 1604
- חומרי עץ יטופלו במעכבי בערה או יסופקו תקנים 921 חלק 6/ 755
- יריעות ובדים יעמדו בת"י 5093
- ליד כל גנראטור יוצב מטפה 6 ק"ג
- בין כל 2 דוכני מזון יוצב מטפה 3 ק"ג-במידה והמרחק עולה על 3.0 מ', יוצב מטפה בכל דוכן
- זיקוקים יאושרו ע"י חבלן משטרת ישראל ורשות הכבאות-בעלי ההיתר יציג תעודת מפעיל
- ארונות כיבוי אש יכילו מזנק, 2 זרנוקים, מתאם ומטפה
- בצדי במה יוצבו מטפים: עד 100 מ"ר במה 2/מעל 100 מ"ר 4
- בכל מבנה אוהל ארעי יוצבו 2 מטפים
- טכנאי גז יאשר מערכות הגז
- מושבים יוצבו בבלוקים של 400 יח' מקס'-כל 4 מושבים יאוזקו, שורה לא תעלה על 40 יח'
- לא יעשה שימוש באש גלויה, גז ופירוטכניקה

הנחיות למתחם הסעדה באירוע

כמות פחים באירוע

חלופה א' : פח אשפה 250 ליטר, 1 מאחרי פוד טראק או 1 לכל 3 דוכנים

חלופה ב' : פח 170 ליטר, בצד הקהל, 1 על כל 2 דוכנים

כמות כיורים לדוכנים באירוע

1 לכל 3 דוכנים או 1 לכל פוד טראק

כמות כיורים לסועדים באירוע מעל 10,000 איש

שוקת של 6-8 ברזים או 6-8 כיורים במערכת סגורה

הנחיות למתחם שירותים באירוע

כמות אסלות וכיורים באירוע

חלופה א' : לפי שטח, לכל 1,000 מ"ר 4 אסלות ו3 כיורים

חלופה ב' : לפי מספר משתתפים

גברים

	אסלות	כיורים
עד 1000 איש	4	4
לכל 600 נוספים	2	1

נשים

	אסלות	כיורים
עד 1000 איש	6	5
לכל 600 נוספים	2	1

תכנית מס':	260513FL	תאריך:	20.05.26
מהדורה מס':	002	קנ"מ:	1:2000\1:200
תאריך האירוע	06.06.26		
מאשר התכנית:	יוסי שמר		
חתימה:	יוסי שמר מורשה נגישות מתו"ס מ.ר. 52502 מורשה נגישות שירות מ.ר. 2337 יוסי שמר מהנדס בטיחות B.SC מ.ר 1806 שמר בטיחות והנדסה אופיר דדון הנדסאי בניין 22350557 דור כובני הנדסאי בניין מ.ר 47025007		

שמר
בטיחות
יועצים
בטיחות לפני הכל